


# URBANIZACIÓN EL GRAN LIMONAR

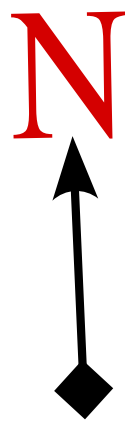


ZONA VERDE

PARQUE

ZONA VERDE

HACIENDA LA GUACA

BARRIO EL PORTAL

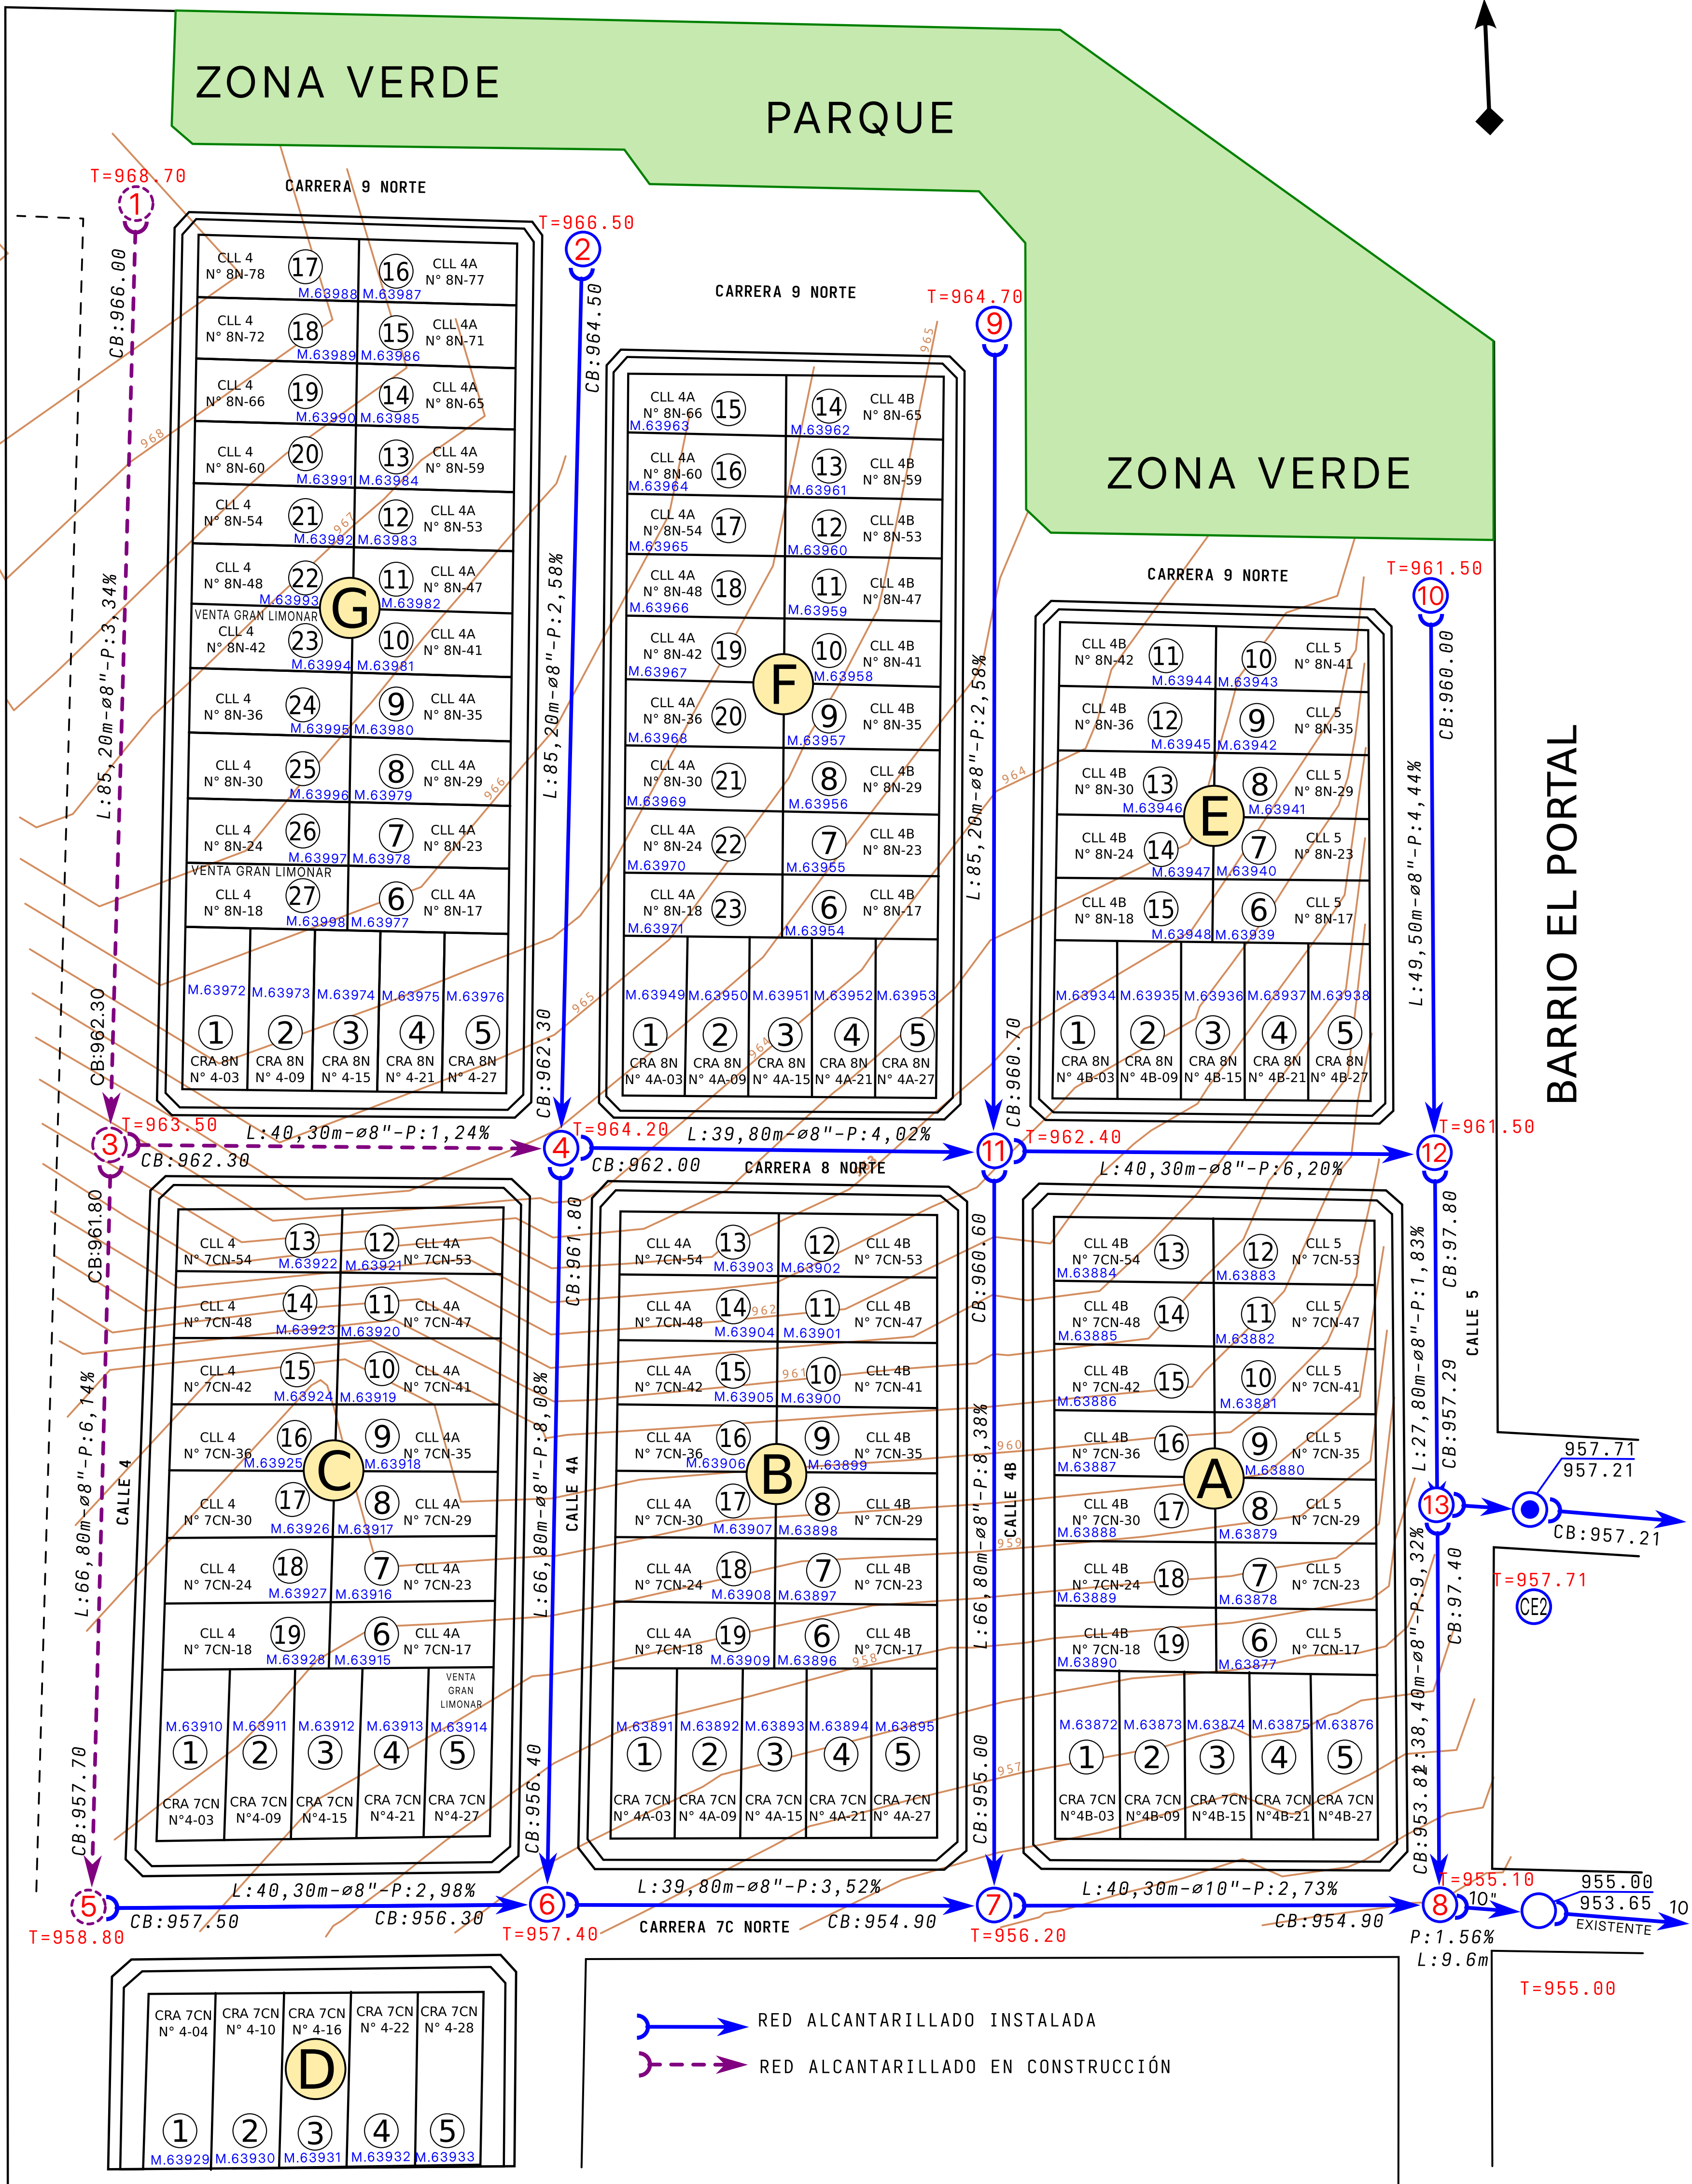

CONTIENE: PLANO COMPLETO "EL GRAN LIMONAR" DE ROLDANILLO VALLE

ELABORÓ: FABIAN ESPAÑA - SECRETARIO J.V.C. EL GRAN LIMONAR

FECHA: 04 MAYO 2026